

Délceg utca 56 - WinWatt modellvizsgálat

Cél: helyiségek és energetikailag releváns határoló szerkezetek visszakövethető ellenőrzése.

Források	É02 földszint, É02B tetőtér, É02C pince, É03 metszetek; 2018-as tanúsítvány a meglévő zónához.
Feldolgozás	Helyi PDF-szöveg- és tervlapolvasás; terv szerinti helyiségterületek; determinisztikus határoló-generálás.
WinWatt rögzítés	32 bites WinWatt import XML -> üres projekt -> mentés -> bezárás/újrainvitás -> natív XML-visszaexport.
Visszaellenőrzés	2 épület, 29 helyiség, 12 szerkezettípus, 78 határoló; területeltérés 0,00 m².
Fontos korlát	A01 a 2018-as tanúsítvány egyetlen aggregált meglévő zónája; részletes meglévő alaprajz hiányában nem bontható tovább.

Jelölési elv az alaprajzokon


A kék címke első sora: helyiségkód, WinWattban rögzített alapterület (A) és belmagasság (h).

A további sorok: szerkezeti kód és a ténylegesen rögzített X×Y méret (X=felület m², Y=darabszám).

R14 = talajon fekvő padló; R1B = új tető; R7 = ferde tető; R5 = új külső fal; R6 = földem; R15/R16 = pincefal.

Szerkezeti döntések

- Külső fal csak olyan helyiséghez került, amely a terv külső kontúrját érinti; belső válaszfal nem lett hamisan külső hőhatároló.
- Minden fűtött helyiséghez alsó és felső hőhatároló került. A tetőtéri helyiségek ferde tetője R7, a pince falai R15/R16.
- Az R1B/R5/R6/R7/R14/R15 U-értékei előzetes rétegtrendi számítások. Anyagkatalógus-rögzítés és nyílászáró-termékadat még külön ellenőrzési lépés.

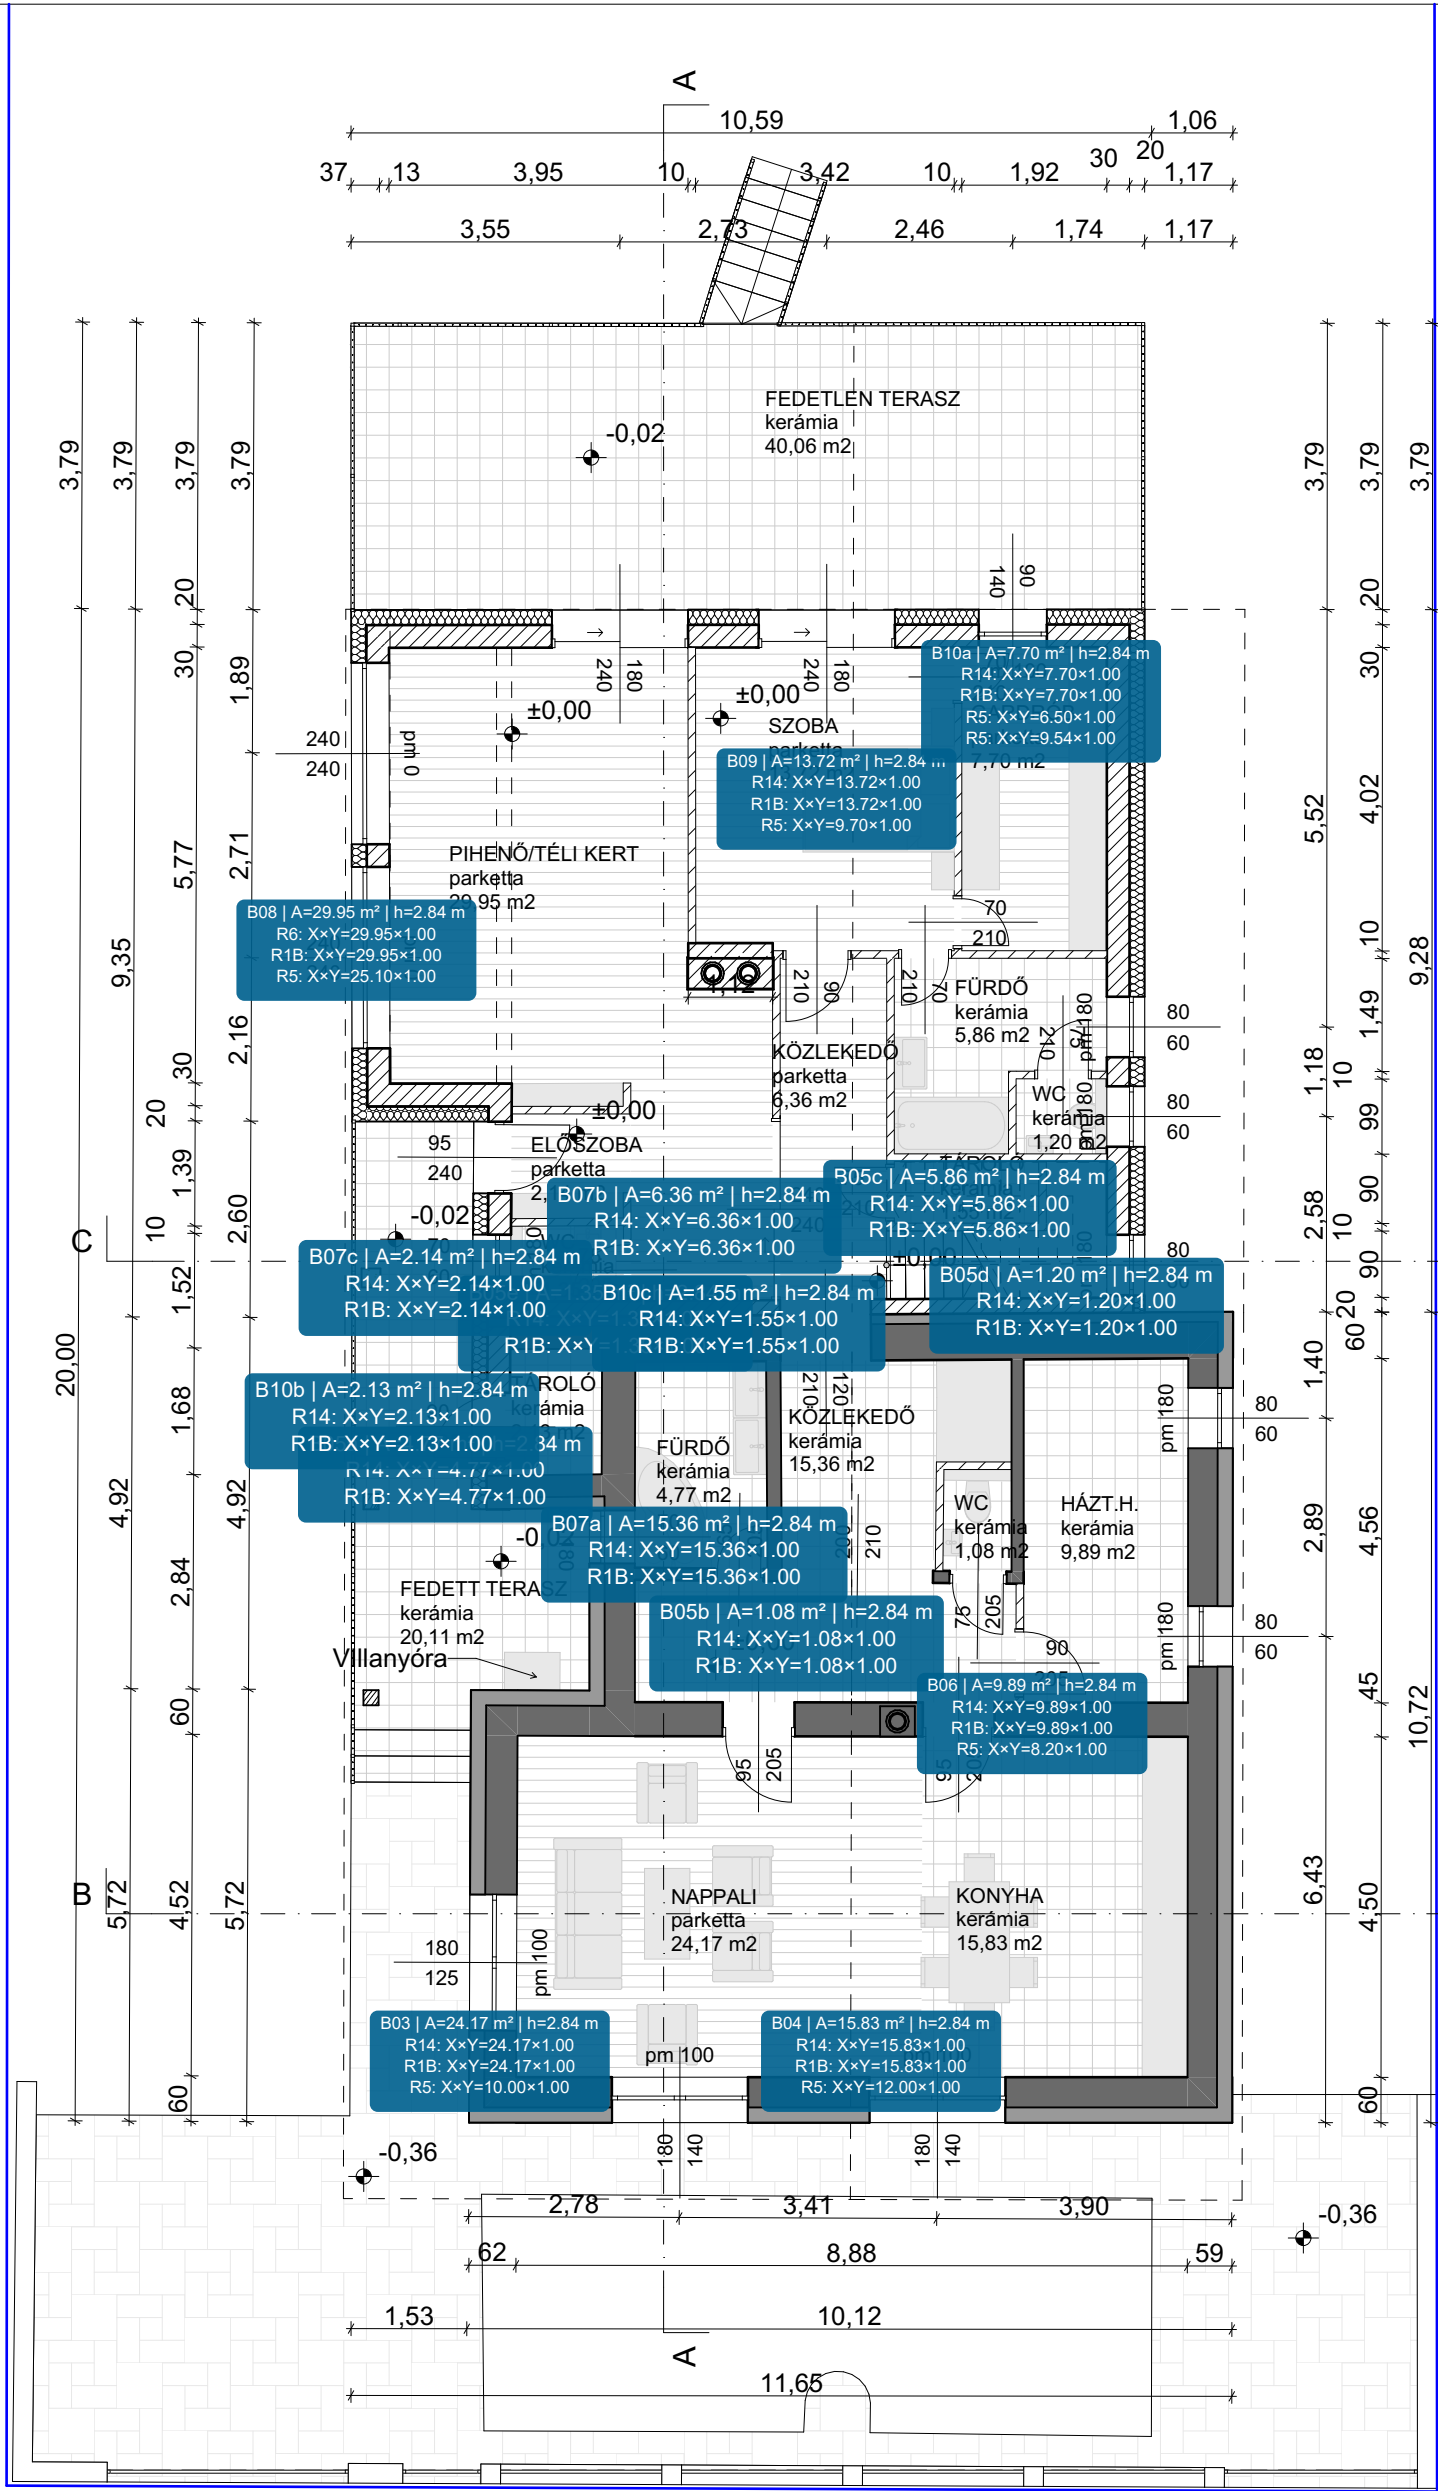


Jelmagyarázat

- Porotherm vázkerámia falazat
- Kőzetgyapot hőszigetelés
- AUSTROTHERM AT H80 homlokzati hőszigetelés
- Lépéshang szigetelés
- Zártcellás hőszigetelés
- Fa
- Estrich aljzatbeton
- Talaj
- Vasbeton
- Kavics
- Meglévő szerkezetek

- a műszaki tervek és egyéb kiadott írásos dokumentációkkal együtt kezelendő!

LAKÓÉPÜLET BŐVÍTÉS EGYSZERŰ BEJELENTÉSI TERVE		
ÉPÍTÉS HELYE:	1162 Budapest, Délceg u. 56. hrsz.: 114403	
ÉPÍTETŐ:	Révész Kornél és Képes Ildikó 1162 Budapest, Délceg u. 56. hrsz.: 114403	
ÉPÍTÉSZ TERVEZŐ:	Godinek Edit É 01-5631 1084 Budapest, Nagy fuvaros utca 22-24 2/21	
2026. 06. 09.	TERVEZETT FÖLDSZINTI ALAPRAJZ M1:100	É-02


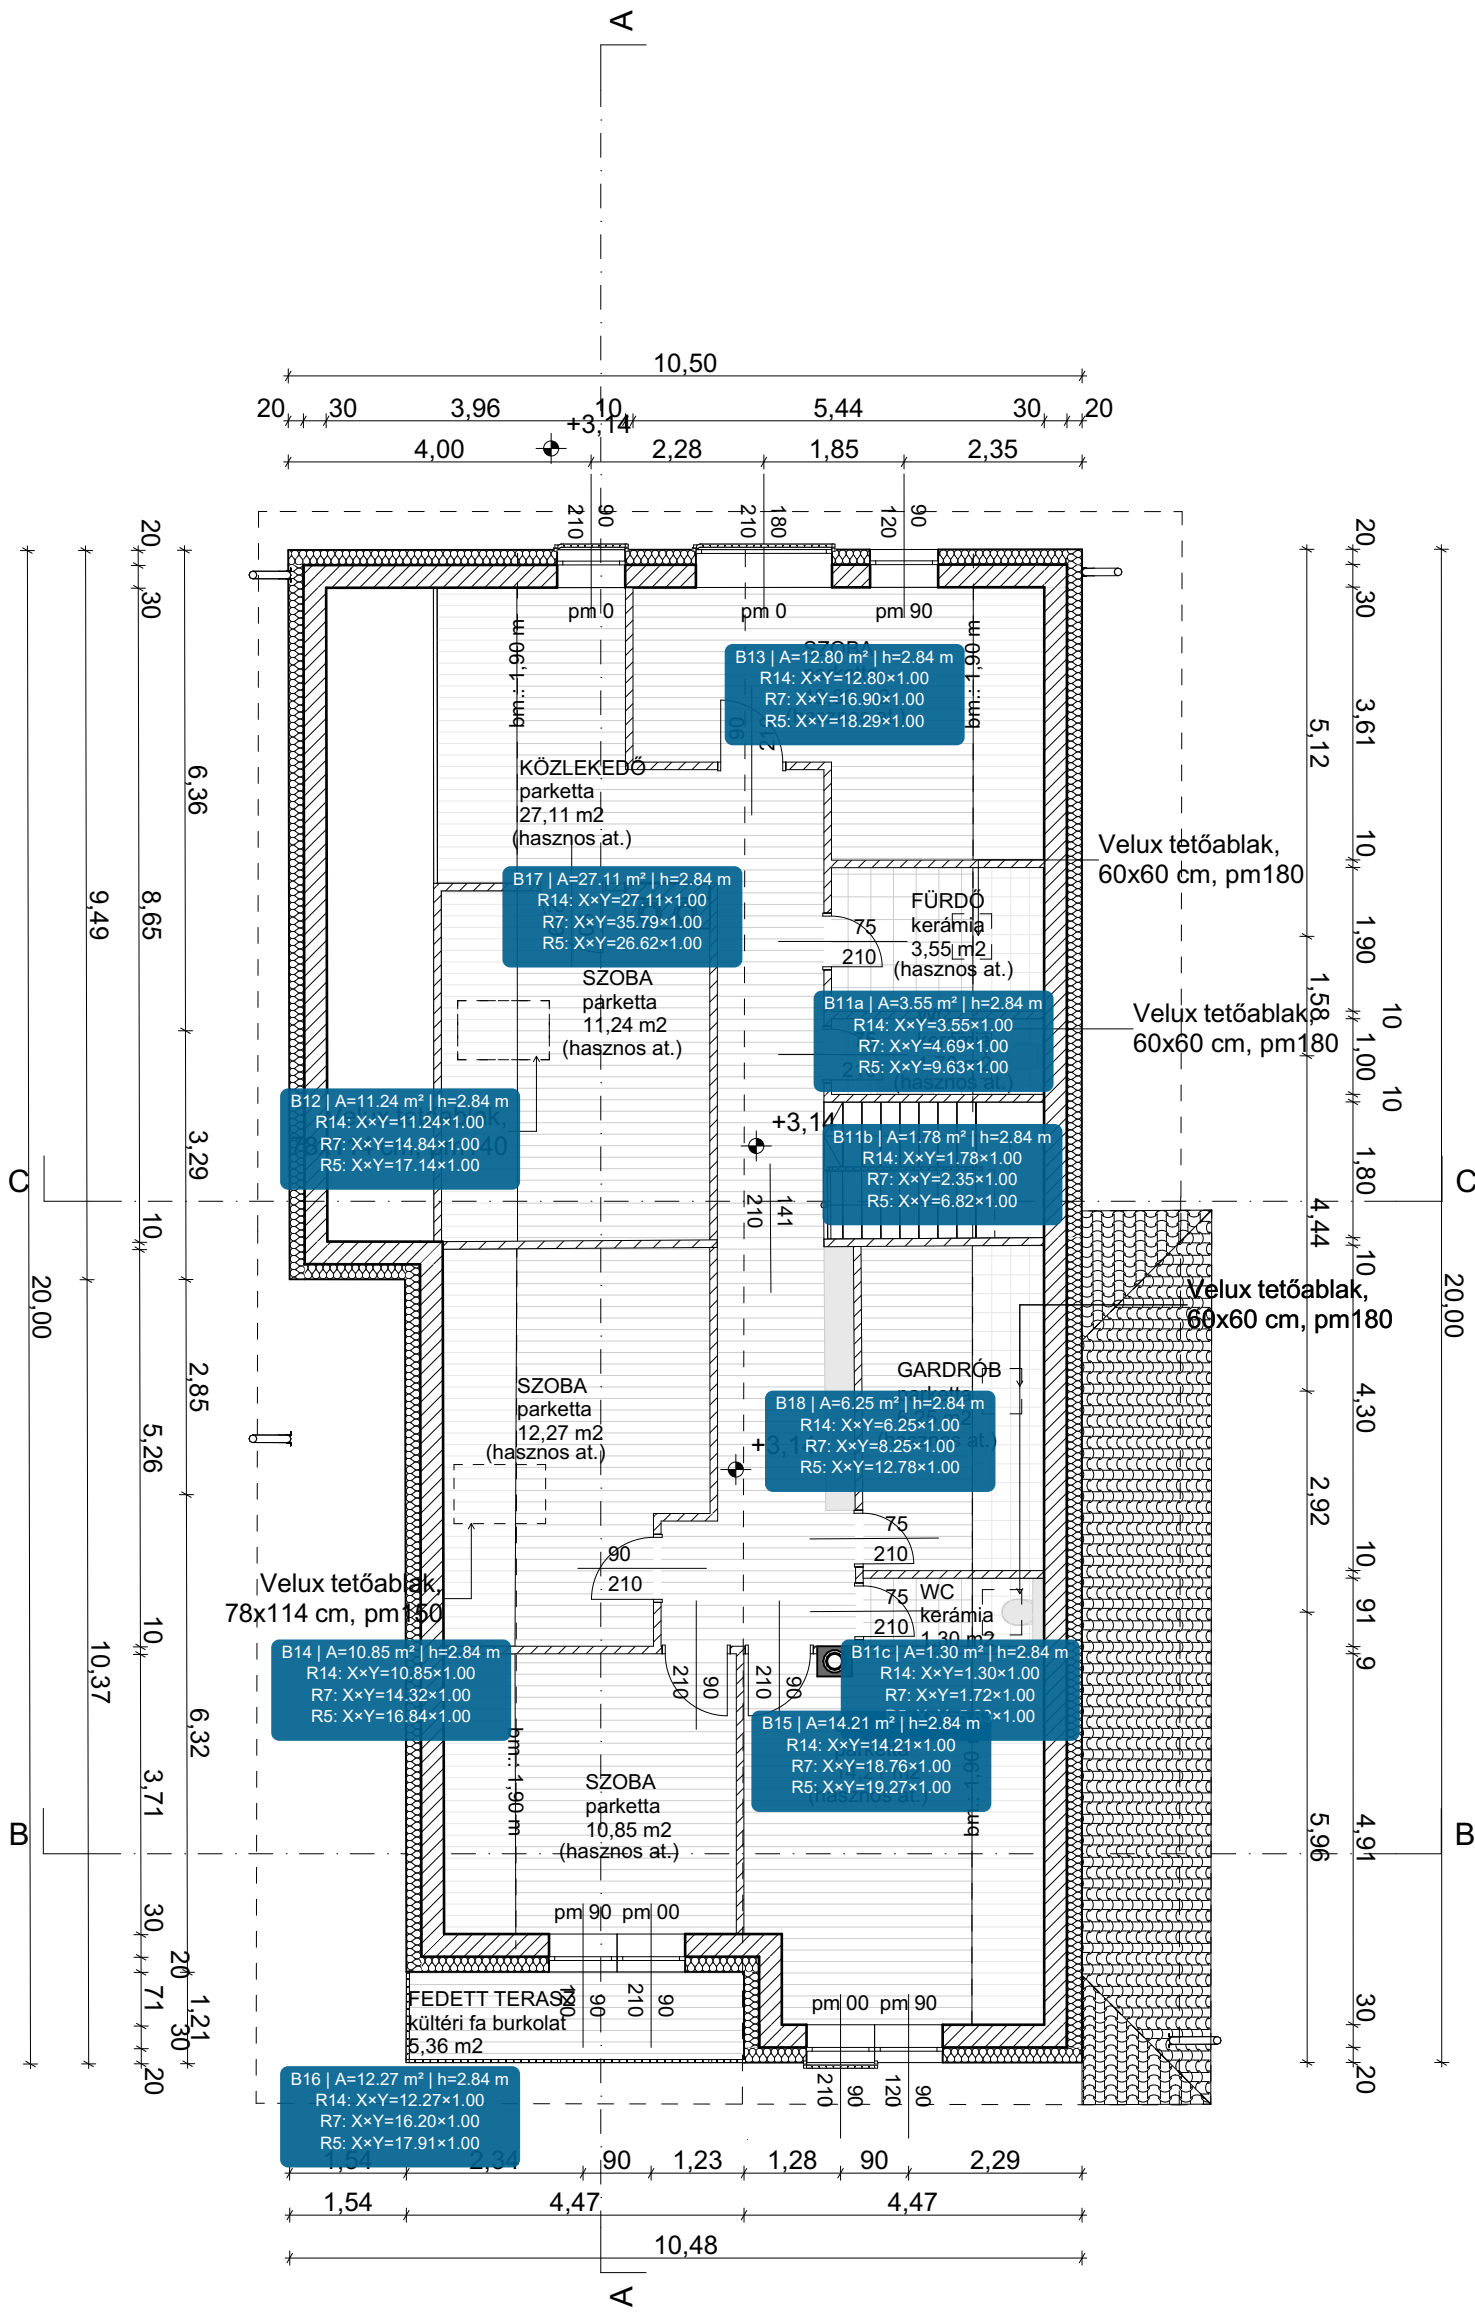


Jelmagyarázat

- Porotherm vázkerámia falazat
- Kőzetgyapot hőszigetelés
- AUSTROTHEM AT H80 homlokzati hőszigetelés
- Lépéshang szigetelés
- Zártcellás hőszigetelés
- Fa
- Estrich aljzatbeton
- Talaj
- Vasbeton
- Kavics

- a műszaki tervek és egyéb kiadott írásos dokumentációkkal együtt kezelendő!

LAKÓÉPÜLET BŐVÍTÉS EGYSZERŰ BEJELENTÉSI TERVE		
ÉPÍTÉS HELYE:	1162 Budapest, Délceg u. 56. hrsz.: 114403	
ÉPÍTETŐ:	Révész Kornél és Képes Ildikó 1162 Budapest, Délceg u. 56. hrsz.: 114403	
ÉPÍTÉSZ TERVEZŐ:	Godinek Edit É 01-5631 1084 Budapest, Nagy fuvaros utca 22-24 2/21	
2026. 05. 12.	TERVEZETT TETŐTÉRI ALAPRAJZ M1:100	É-02B

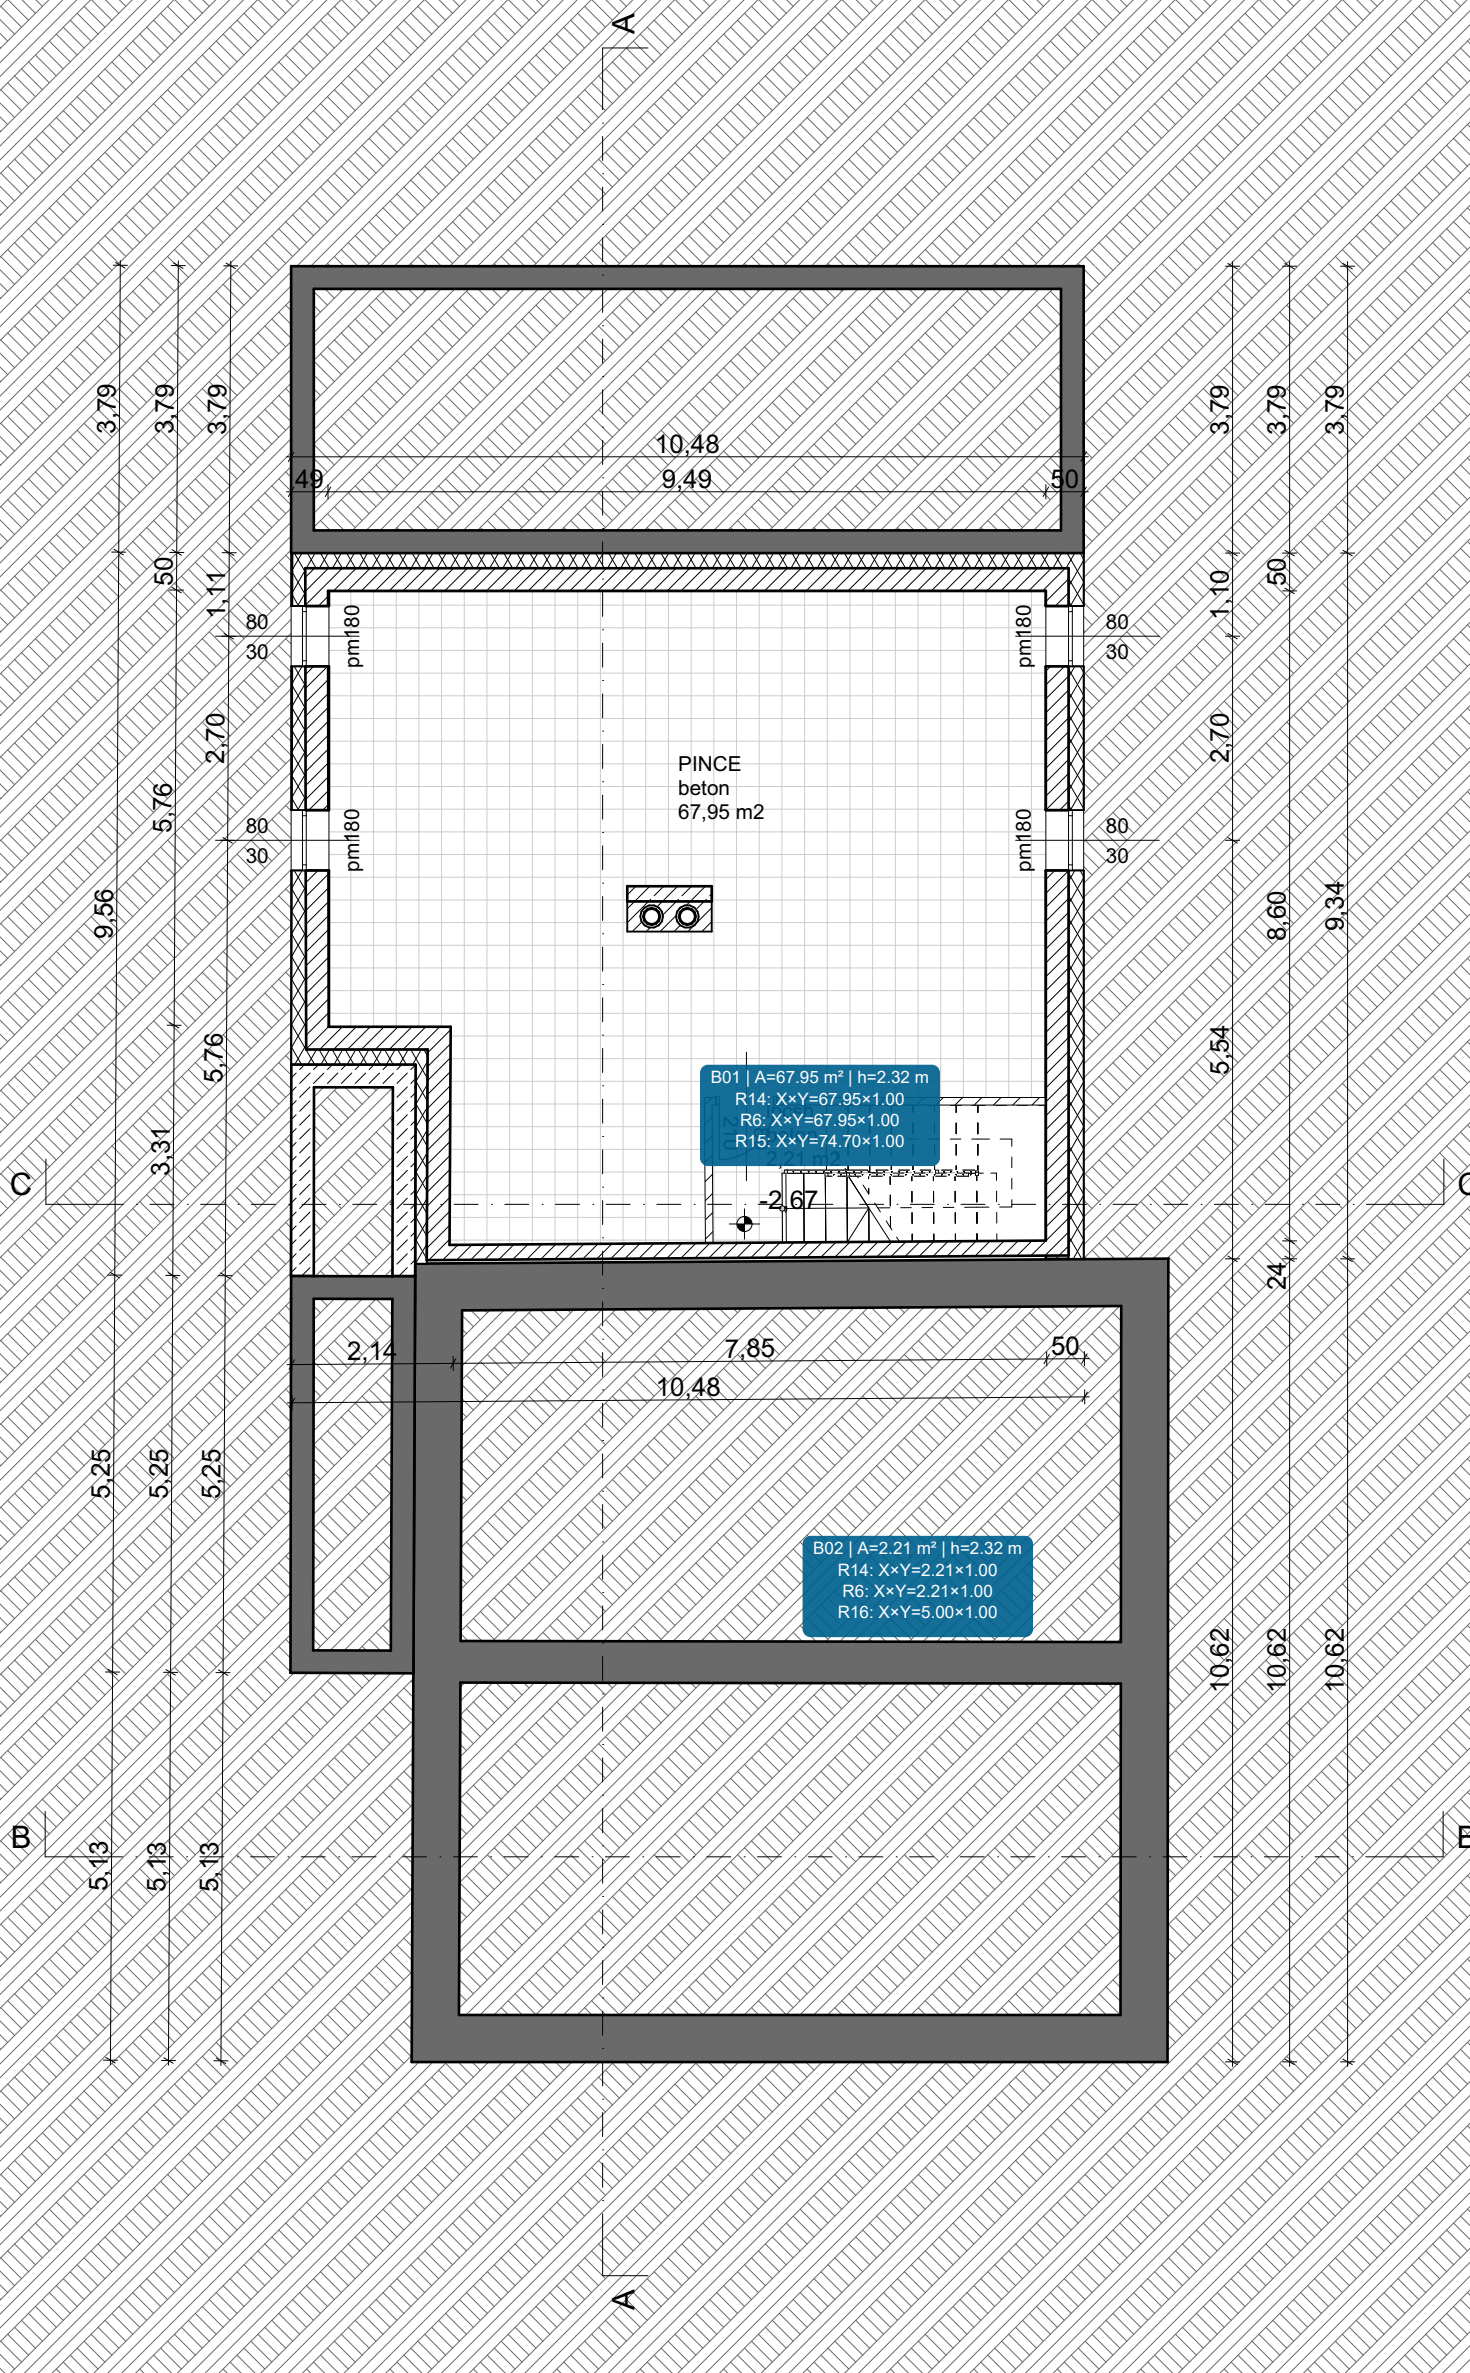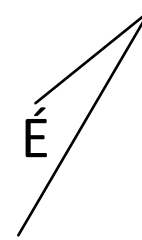

Jelmagyarázat

- Porotherm vázkerámia falazat
- Kőzetgyapot hőszigetelés
- AUSTROTHEM AT H80 homlokzati hőszigetelés
- Lépéshang szigetelés
- Zártcellás hőszigetelés
- Fa
- Estrich aljzatbeton
- Talaj
- Vasbeton
- Kavics
- Meglévő szerkezetek

- a műszaki tervek és egyéb kiadott írásos dokumentációkkal együtt kezelendő!

LAKÓÉPÜLET BŐVÍTÉS EGYSZERŰ BEJELENTÉSI TERVE

ÉPÍTÉS HELYE:	1162 Budapest, Délceg u. 56. hrsz.: 114403	
ÉPÍTETŐ:	Révész Kornél és Képes Ildikó 1162 Budapest, Délceg u. 56. hrsz.: 114403	
ÉPÍTÉSZ TERVEZŐ:	Godinek Edit É 01-5631 1084 Budapest, Nagy fuvaros utca 22-24 2/21	
2026. 07. 30.	TERVEZETT PINCESZINTI ALAPRAJZ M1:100	É-02C