
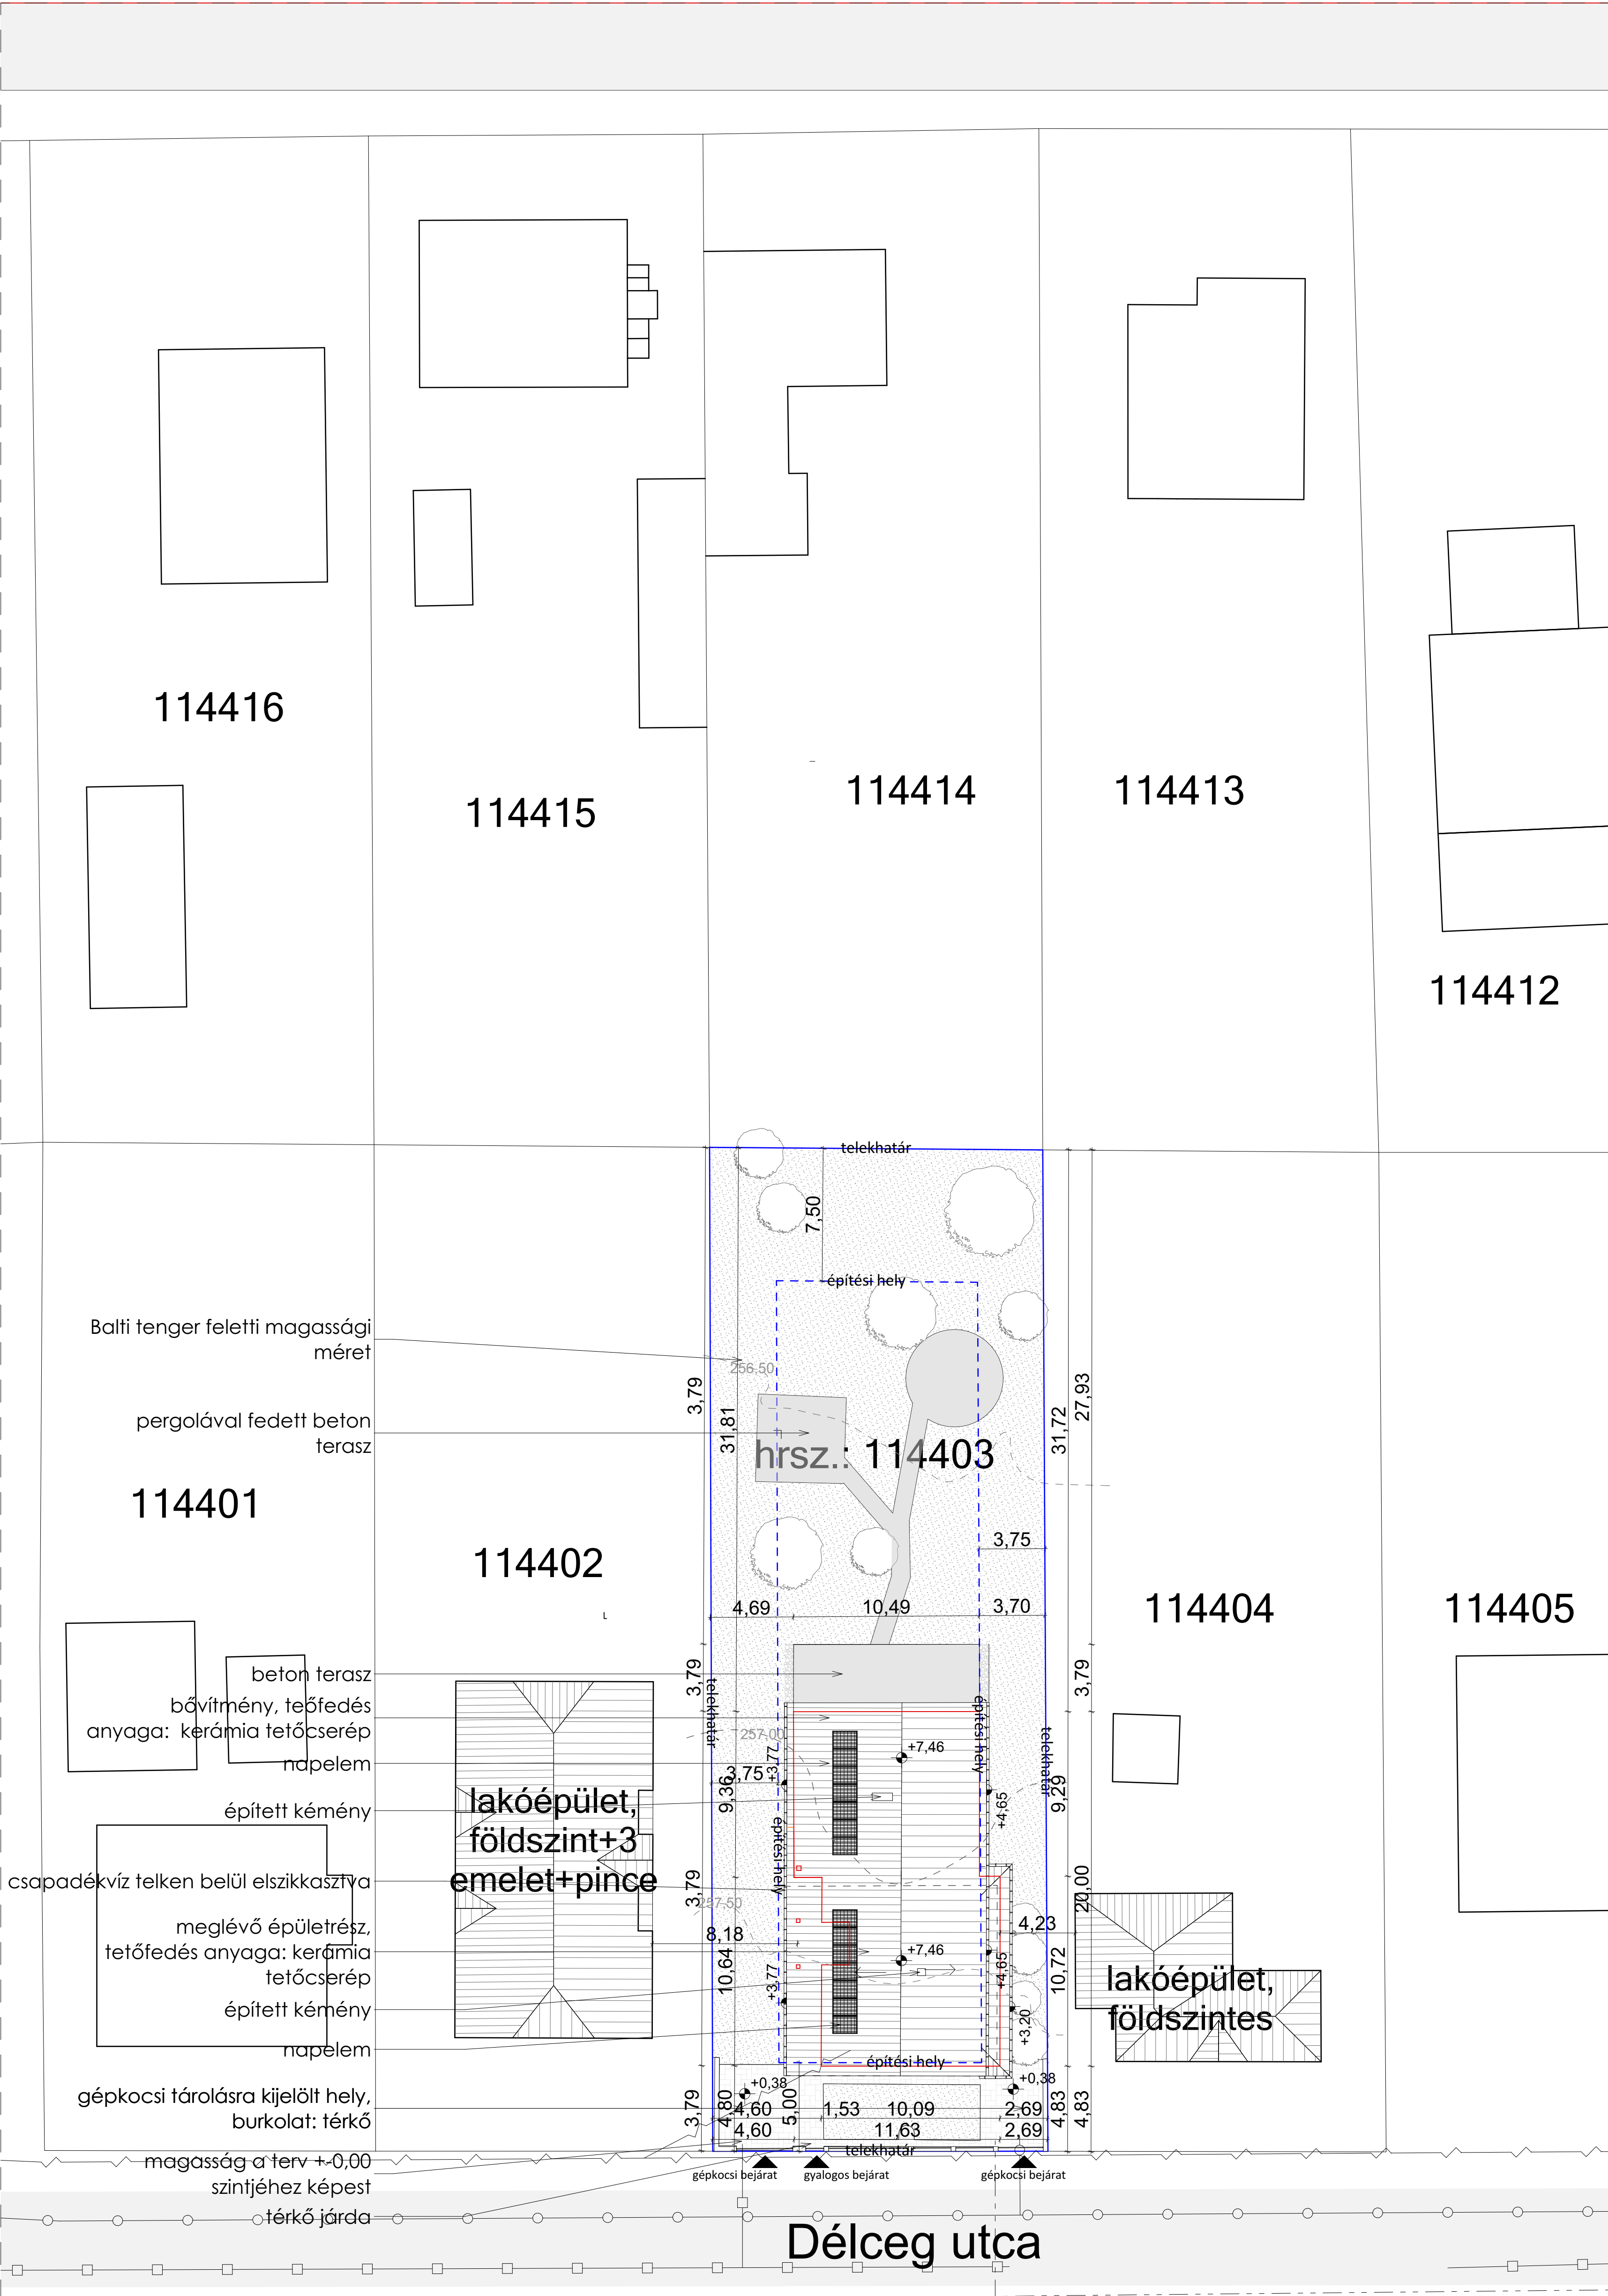


Építési övezet:	Lf-1	
Beépítési mód:	szabadon álló	
Telek területe	1067	m ²
Bruttó beépített terület:	220,10	m ²
Burkolt felület:	194,70	m ²
Összesen:	414,80	m ²
Maximális beépítési százalék	25	%
Beépítési százalék	20,63	%
Minimális zöldfelület	60	%
Zöldfelület	652,20	m ²
Zöldfelületi mutató	61,12	%
Ereszmagassága:	+3,77,+4,65 m	
Gerincmagasság:	+7,46 m	
Megengedett épületmagasság	7,50	m
Épületmagasság	5,40	m
Földszinti padlószint	+0,00 m	
A terv +0,00 szintjének Balti tenger feletti magassága: 258,00 mBf		
Csatorna	0,6 m3 /nap	NA150 KG PVC
Víz	0,6m3/ nap	D25 mm KPE bekötéssel
Elektromos áram	0,4 KWH,	
hálózati feszültség	220/380 V	
Gáz	4m3/ óra	32mm KPE bekötéssel

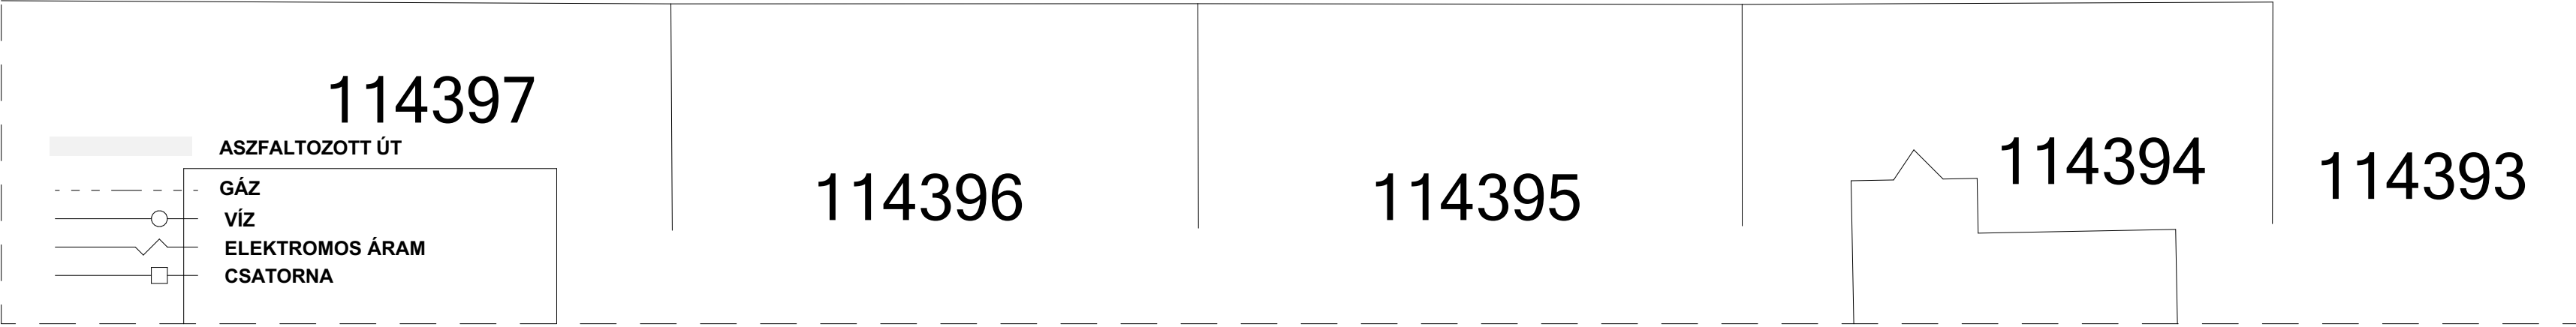

- a műszaki tervek és egyéb kiadott írásos dokumentációkkal együtt kezelendő!		
LAKÓÉPÜLET EGYSZERŰ BEJELENTÉSI TERVE		
ÉPÍTÉS HELYE:	1162 Budapest, Délceg u. 56. hrsz.: 114403	
ÉPÍTETŐ:	Révész Kornél és Képes Ildikó 1162 Budapest, Délceg u. 56. hrsz.: 114403	
ÉPÍTÉSZ TERVEZŐ:	Godinek Edit É 01-5631 1084 Budapest, Nagy fuvaros utca 22-24 2/21	
2026. 05. 12.	TERVEZETT HELYSZÍNRAJZ M1:200	É-01