
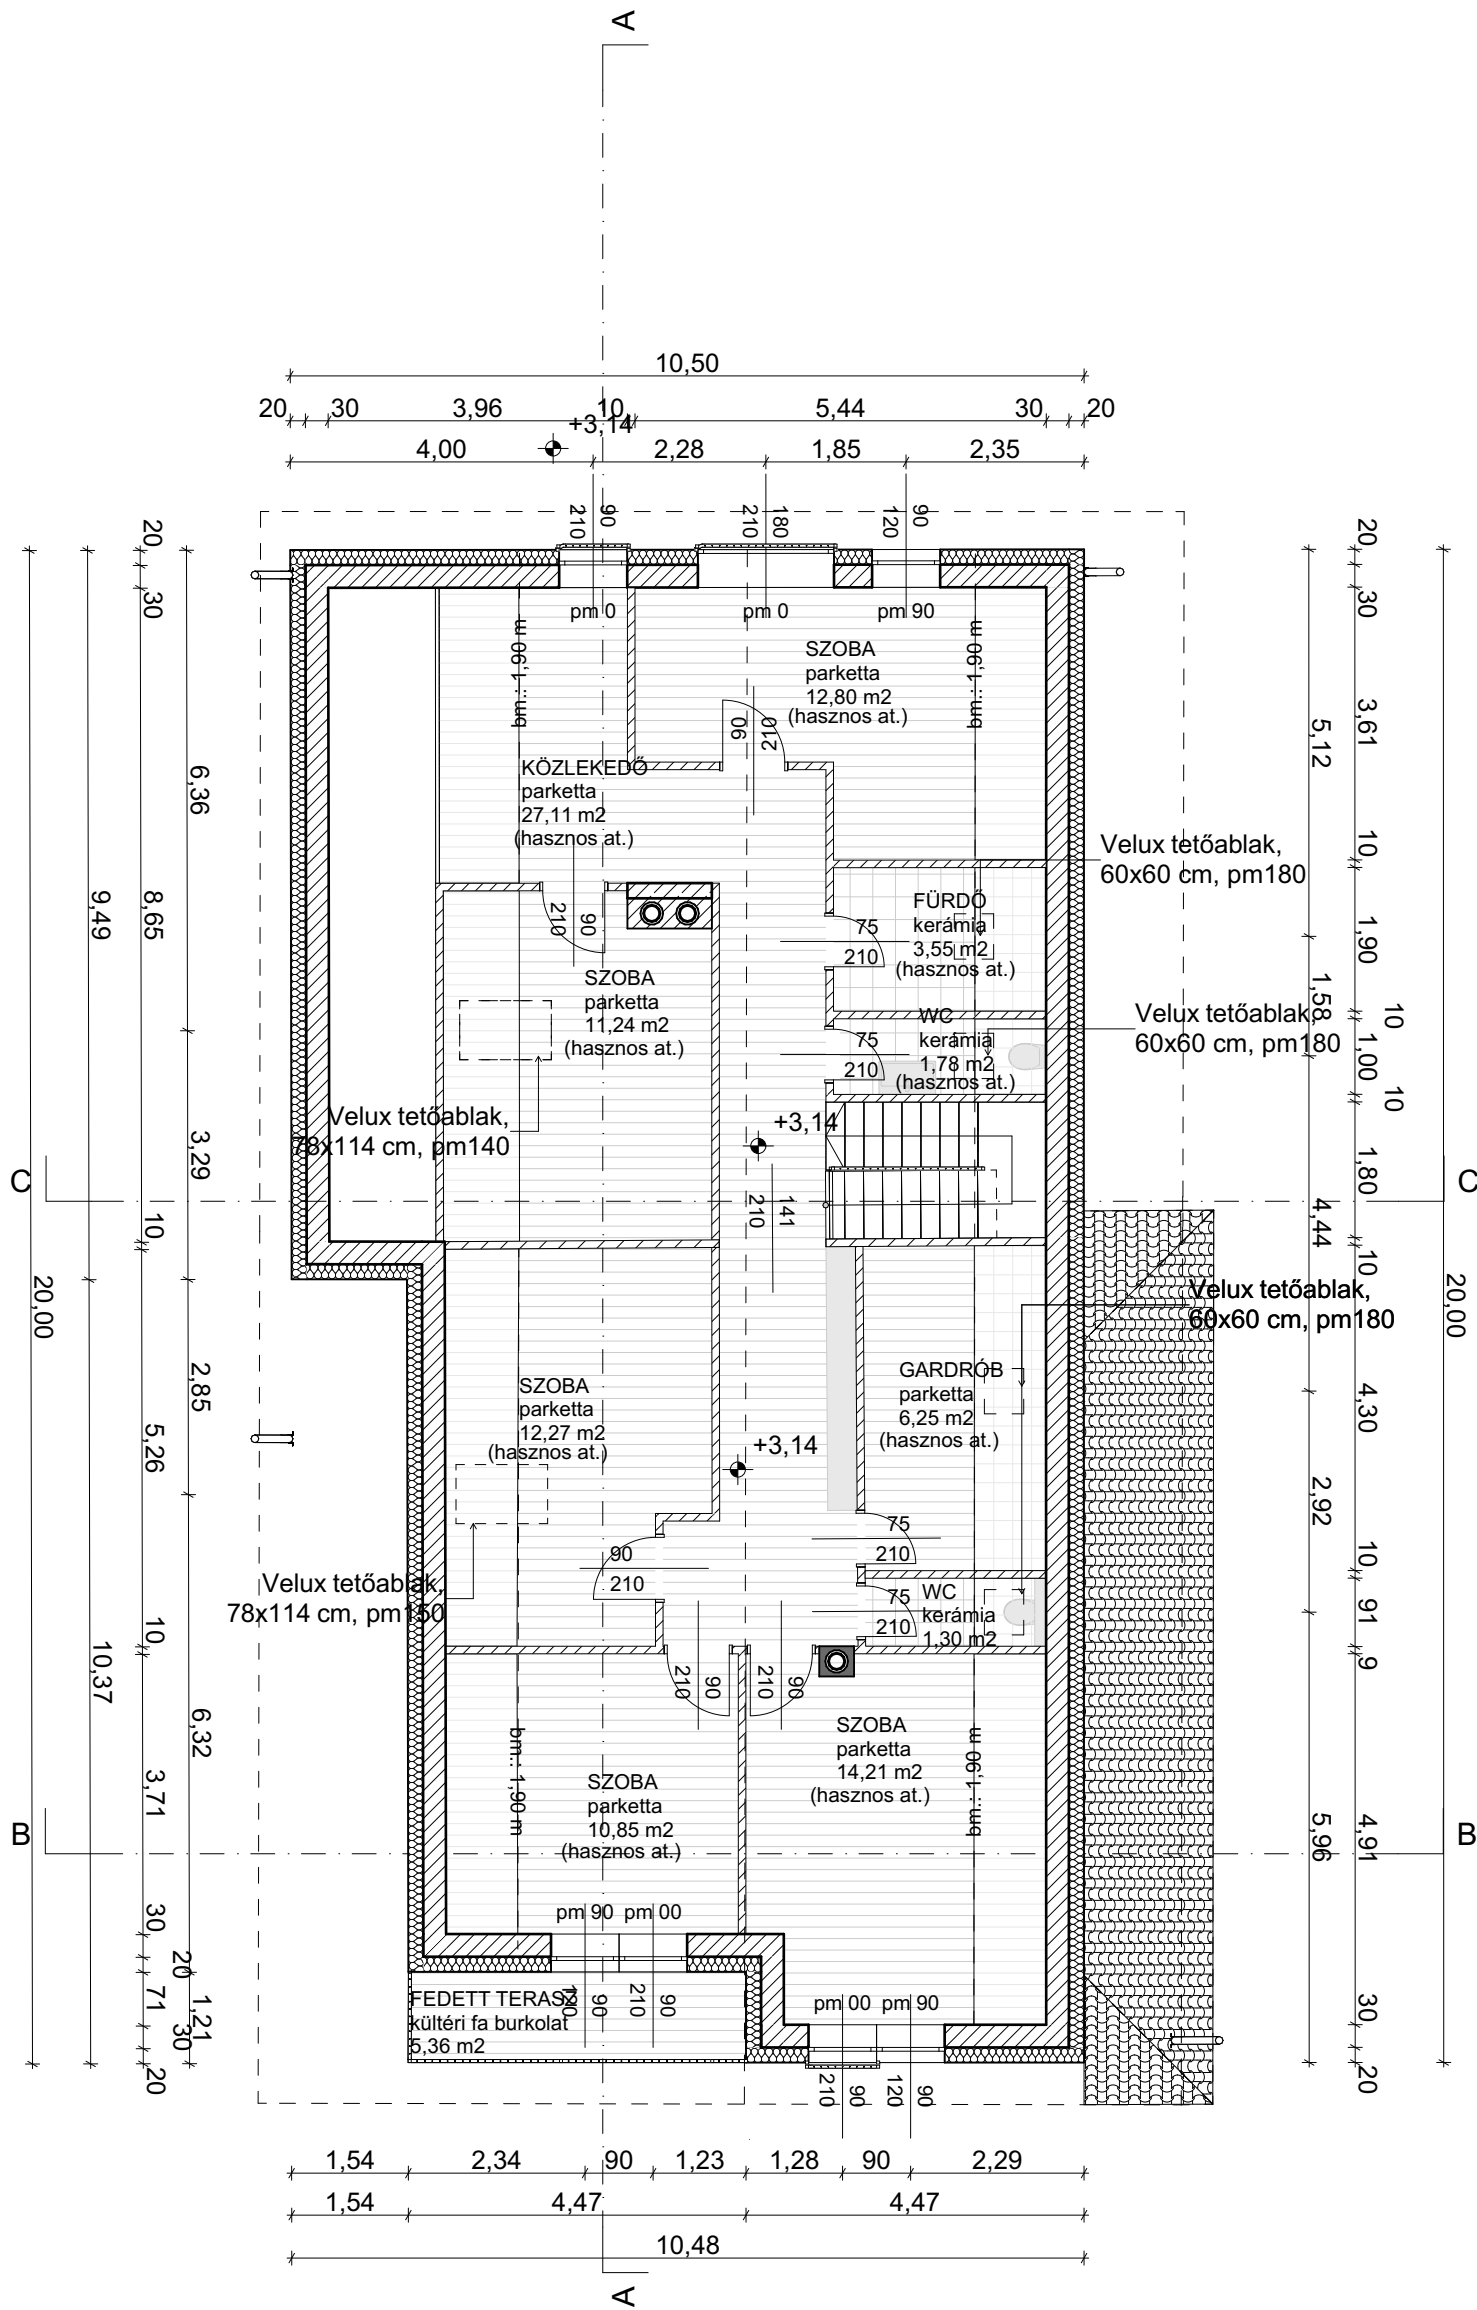


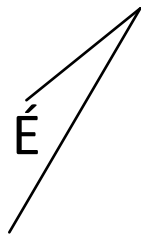

Jelmagyarázat

- Porotherm vázkerámia falazat
- Kőzetgyapot hőszigetelés
- AUSTROTHEM AT H80 homlokzati hőszigetelés
- Lépéshang szigetelés
- Zártcellás hőszigetelés
- Fa
- Estrich aljzatbeton
- Talaj
- Vasbeton
- Kavics

- a műszaki tervek és egyéb kiadott írásos dokumentációkkal együtt kezelendő!

LAKÓÉPÜLET BŐVÍTÉS EGYSZERŰ BEJELENTÉSI TERVE		
ÉPÍTÉS HELYE:	1162 Budapest, Délceg u. 56. hrsz.: 114403	
ÉPÍTETŐ:	Révész Kornél és Képes Ildikó 1162 Budapest, Délceg u. 56. hrsz.: 114403	
ÉPÍTÉSZ TERVEZŐ:	Godinek Edit É 01-5631 1084 Budapest, Nagy fuvaros utca 22-24 2/21	
2026. 05. 12.	TERVEZETT TETŐTÉRI ALAPRAJZ M1:100	É-02B