




B-B METSZET

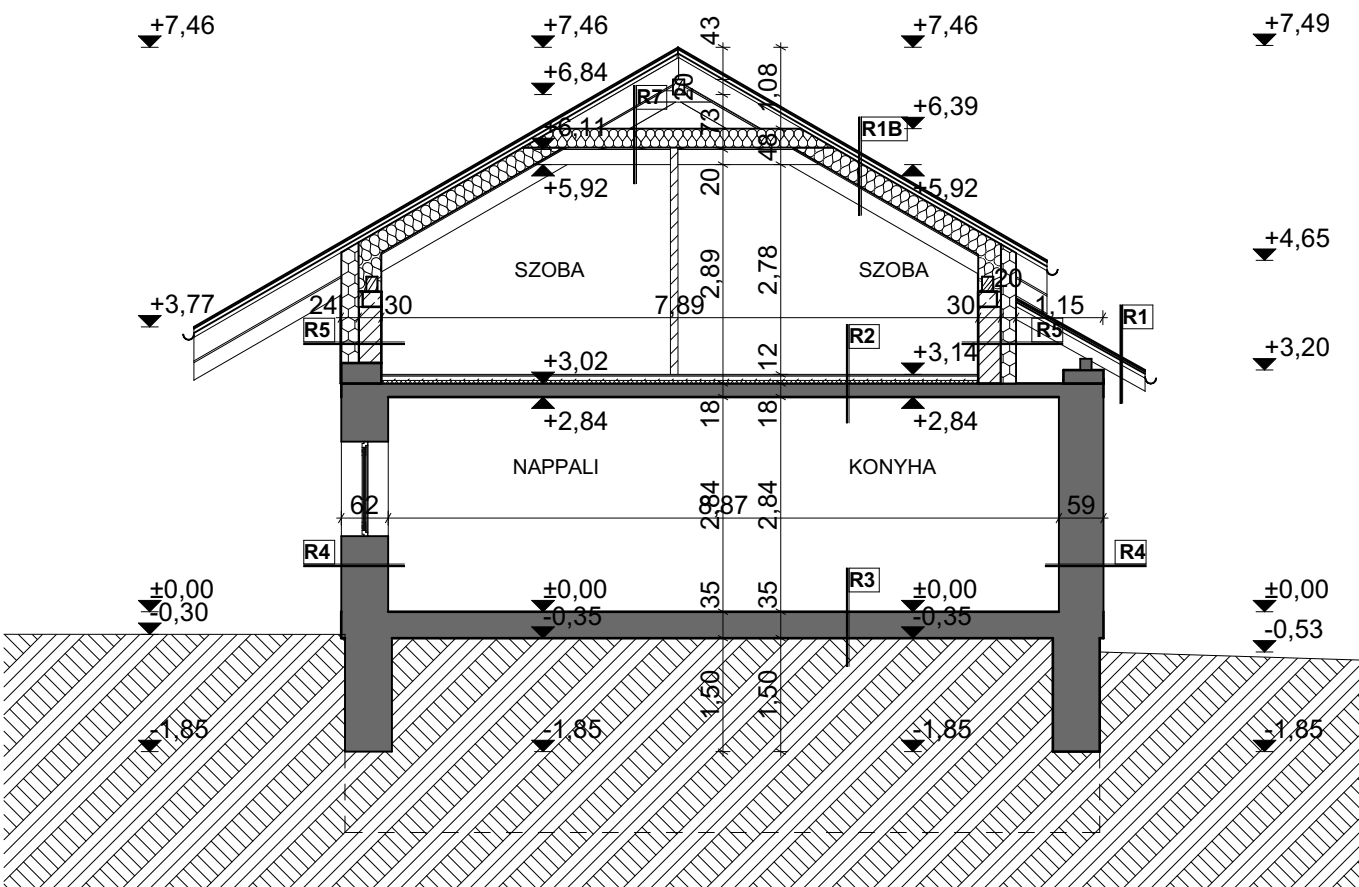

C-C METSZET

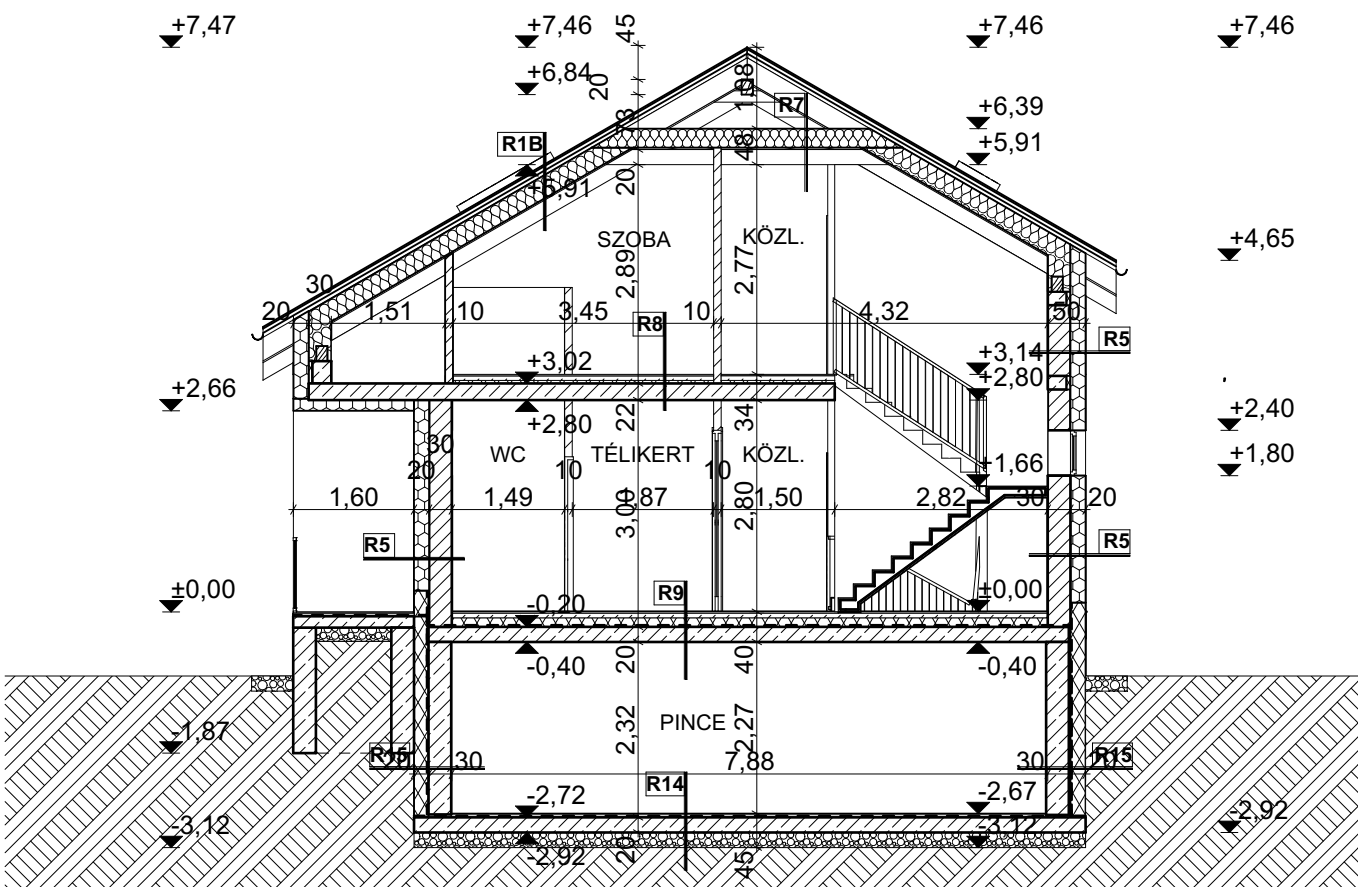

A-A METSZET

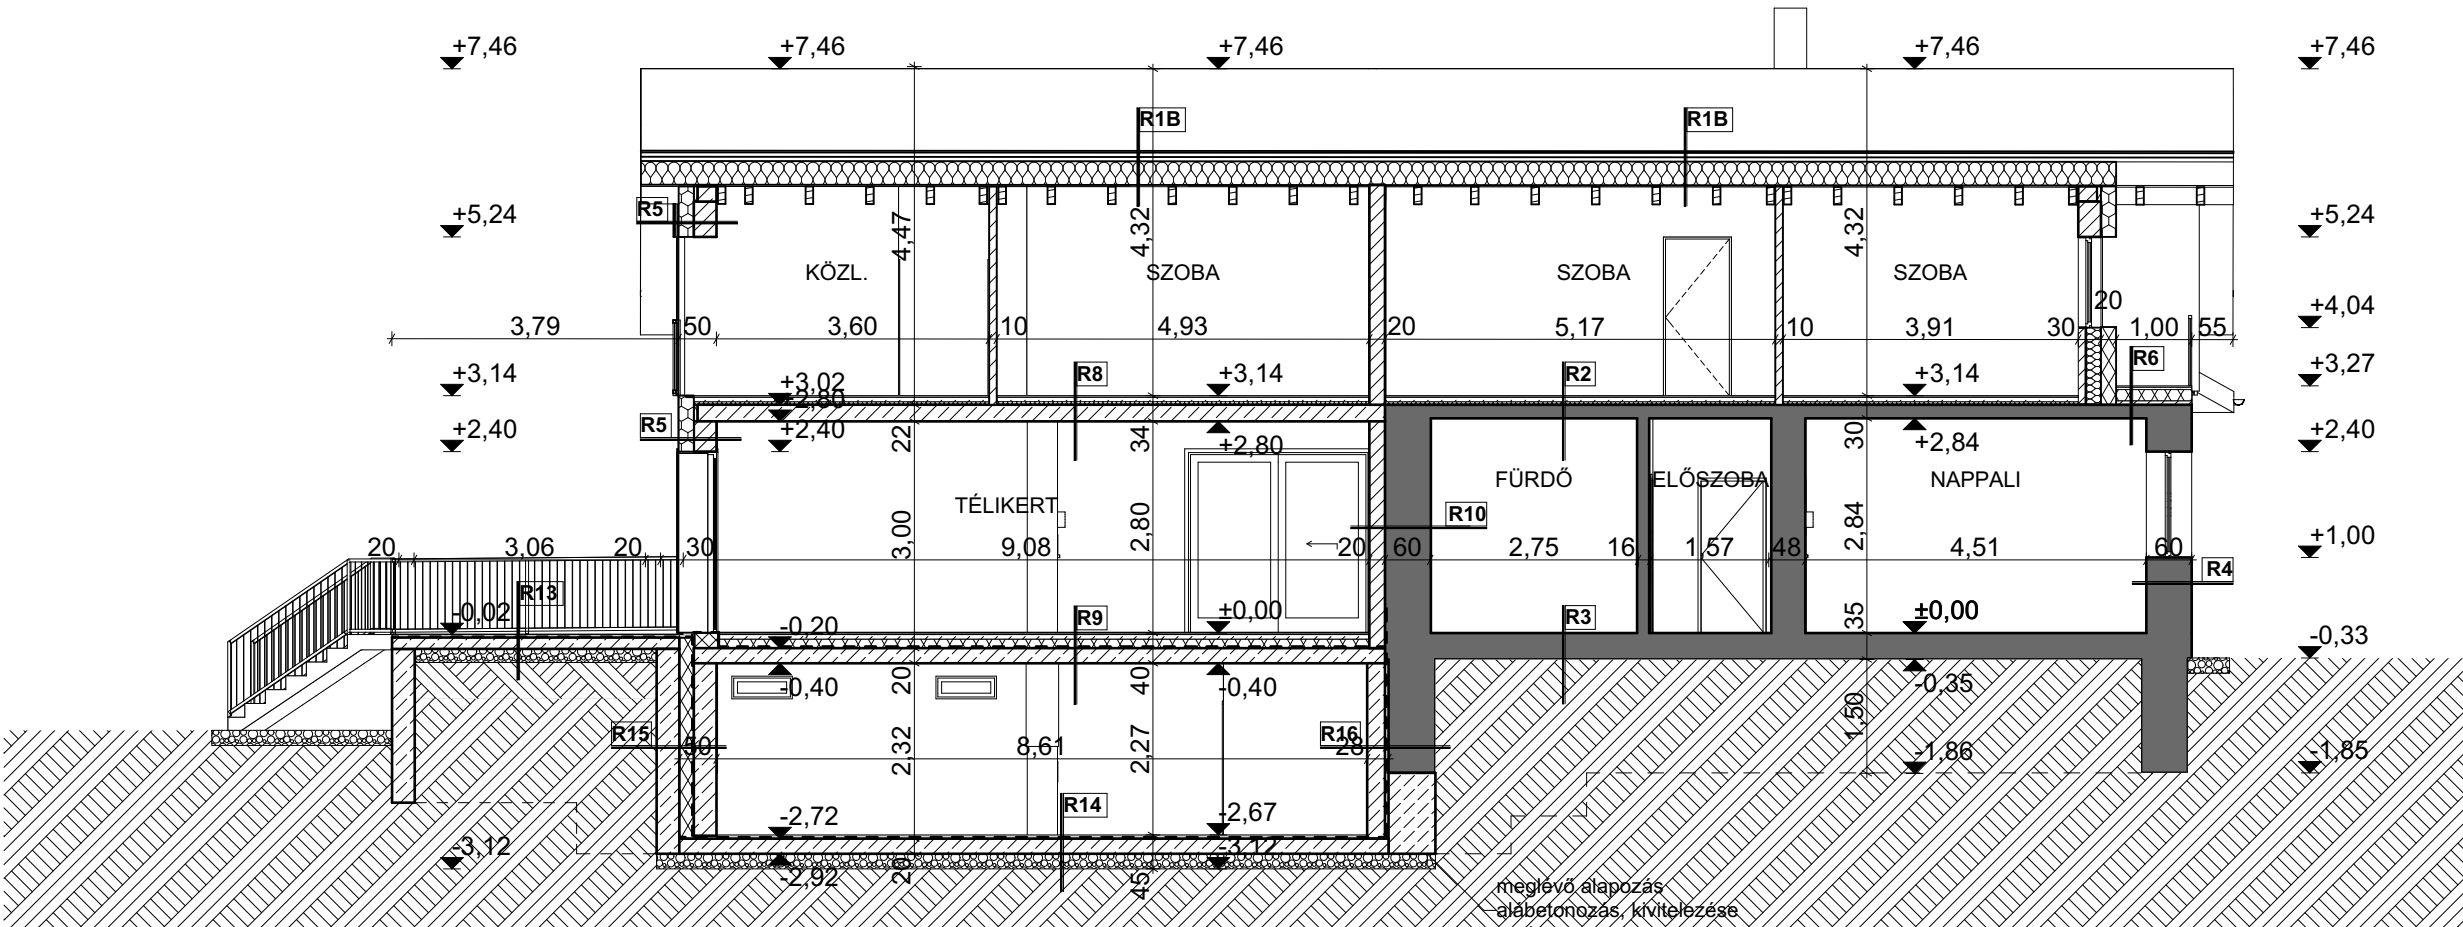

Jelmagyarázat

- Porotherm vázkerámia falazat
- Kőzetgyapot hőszigetelés
- AUSTROTHERM AT H80 homlokzati hőszigetelés
- Lépéshang szigetelés
- Zártcellás hőszigetelés
- Fa
- Estrich aljzatbeton
- Talaj
- Vasbeton
- Kavics

RÉTEGRENDEK

R1./ Tető:

- 1 rtg. Kerámia tetőcserép fedés
- 2,5/5,0 cm Tetőléc
- 1 rtg. Szélzáró, Páraáteresztő fólia
- 2,5/5,0 cm Ellenléc
- 10/15 cm Szarufa
- Kiszellőztetett padlástér

R2./Padlásfödém:

- 2 cm Padlóburkolat + rag
- 6,0 cm Estrich aljzatbeton
- 1 rtg. techn. szig PE fólia
- 4,0 cm lépésálló hőszigetelés
- Meglévő födémszerkezet
- Belső felületképzés

R3./ Talajon fekvő padló

Meglévő rétegrend

R4./ Homlokzati fal:

Meglévő rétegrend

- R5./ Homlokzati fal
- 1 rtg. külső oldali glettelés+festés
 - 20 cm AUSTROTHERM AT H80 homlokzati hőszigetelés
 - 1 rtg. Légzáró vakolat
 - 30 cm Porotherm 38 vázkerámia falazat
 - 1 rtg. belső oldali vakolat+festés

- R6./Tetőterasz
- 2 cm WPC burkolat fa hatású
 - 3 cm Bazaltúzalék ágyazóréteg
 - 1 rtg. Szűrő-elválasztó réteg
 - 2 rtg. Bitumenes vízszigetelés
 - 15,0 cm PUR hőszigetelés
 - 2-5 cm Lejtést adó beton
 - Meglévő födémszerkezet
 - Belső felületképzés

- R7./ Padlás
- Kiszellőztetett padlástér
 - 1 rtg. Páraáteresztő fólia
 - 25 cm kőzetgyapot hőszigetelés
 - 1 rtg. Párazáró fólia
 - 2 rtg. tűzgátló gipszkarton
 - Fogópár

- R8./ Közbenső födémszerkezet
- 2 cm Padlóburkolat + rag
 - 6,0 cm Estrich aljzatbeton
 - 1 rtg. techn. szig PE fólia
 - 4,0 cm lépésálló hőszigetelés
 - 20 cm Monolit vasbeton födémszerkezet
 - Belső felületképzés

- R9./ Közbenső födémszerkezet
- 2 cm Padlóburkolat + rag
 - 6,0 cm Estrich aljzatbeton
 - 1 rtg. techn. szig PE fólia
 - 12 cm lépésálló hőszigetelés
 - 20 cm Monolit vasbeton födémszerkezet
 - Belső felületképzés

- R10./Közbenső fal fal
- 1 rtg. belső oldali vakolat+festés
 - 20 cm Porotherm 38 vázkerámia falazat
 - Dilatációs hézag
 - Meglévő falazat
 - 1 rtg. belső oldali vakolat+festés

- R13./Terasz
- 2 cm fagyálló kerámia burk.+rag.
 - Aljzatbeton lejtésben
 - 2 rtg. kenhető vízszigetelés
 - 15 cm vasalt aljzatlemez
 - 20 cm tömörített kavics ágyazat

- R1B./ Új tetőszerkezet
- 1 rtg. kerámia cserépfedés
 - 30/50 tetőléc gomba-, rovar- és lángmentesített
 - 50/75 ellenléc omiba-, rovar- és lángmentesített
 - 1 rtg. szél- és vízzáró, hőszigetelésre integrált páraáteresztő alátétfólia
 - 25 cm PIR hőszigetelés lépcsős ütközőhézagú, ellenléceken keresztül borovi fenyő szaruzathoz vonal mentén leszorítva
 - 1 rtg. lég- és párazáró polietilén fólia, egymáshoz és szilikát szerkezetekhez ragasztósávval felületfolytonosítva, sd>500m
 - 2.5 cm gomba-, rovar- és lángmentesített horonyeresztékes gyalult első osztályú deszka burkolat
 - 10/15 omiba-, rovar- és lángmentesített méretezett borovi szaruzat

- R14./ Talajon fekvő padló
- 5 cm szigetelést védő beton
 - 1 rtg. min. 4,5 mm vastag VILLAS VILLAVERDE WS-I 4éves FLL gyökérálló minősítésű mod.bit. vastaglemez vízszigetelés felső rtg. átlapolással lángolvasztva
 - 1 rtg. min. 4,0 mm vastag VILLAS E-G 45 F/K SBS modifikált bit. vastaglemez alsó réteg teljes felületén lángolvasztással ragasztva
 - 1 rtg. Icopal ELASTO-PRIMER vizes bázisú hideg bitumenmáz kellősítés
 - 25 cm monolit vasbeton lemezalap
 - 25 cm kavicsfeltöltés

- R15./ Pincefal
- Talajfeltöltés/Terasz alaptest
 - 20 cm XPS hőszigetelés
 - 2 rtg. Villas OV4F/K bitumenes szigetelő lemez
 - 1 rtg. Icopal rapid kellősítés
 - 1 rtg. légzáró vakolat
 - 30 cm zsalukő falazat
 - 1 rtg. légzáró vakolat 1 rtg
 - 1 rtg. belső felületképzés

- R16./ Pincefal
- Meglévő épület alaptest
 - Felületkiegénylítés
 - 1 rtg. Icopal rapid kellősítés
 - 2 rtg. Villas OV4F/K bitumenes szigetelő lemez
 - 25 cm zsalukő falazat
 - 1 rtg. légzáró vakolat 1 rtg
 - 1 rtg. belső felületképzés

- a műszaki tervek és egyéb kiadott írásos dokumentációkkal együtt kezelendő!

LAKÓÉPÜLET BŐVÍTÉS EGYSZERŰ BEJELENTÉSI TERVE		
ÉPÍTÉS HELYE:	1162 Budapest, Délceg u. 56. hrsz.: 114403	
ÉPÍTETŐ:	Révész Kornél és Képes Ildikó 1162 Budapest, Délceg u. 56. hrsz.: 114403	
ÉPÍTÉSZ TERVEZŐ:	Godinek Edit É 01-5631 1084 Budapest, Nagy fuvaros utca 22-24 2/21	
2026. 07. 30.	TERVEZETT METSZETEK M1:100	É-03